
SITE PLAN SHOWING EXISTING VILLA NO. A-0060 BLOCK -A ICON VILLA, SUSHANT CITY BY ANSAL API VILLAGE CHANDIYAWAS, GEGAL, NH-8 JAIPUR ROAD AJMER,

EXECUTANT :-

CLAIMANT :-

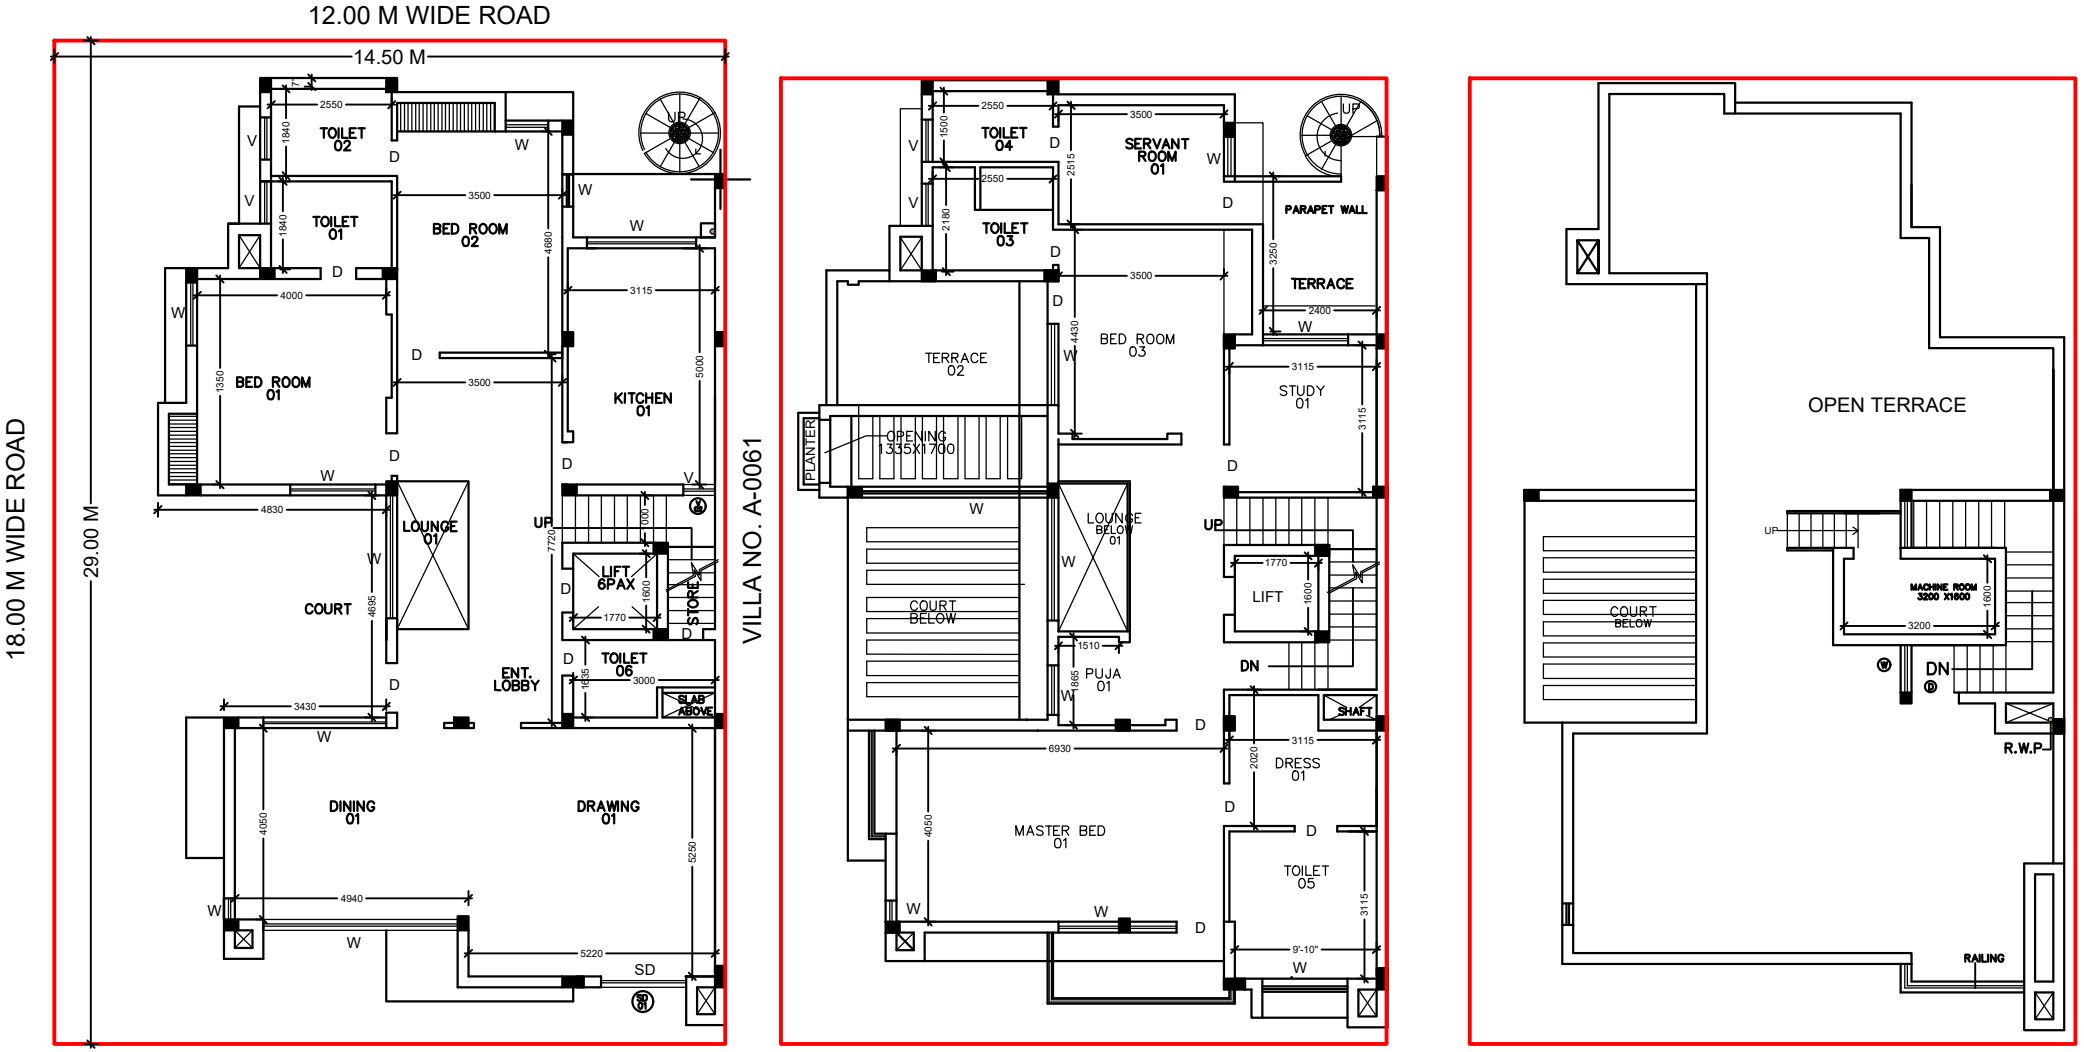

NOTE :-

LAND AREA = 420.50 SQ.M.

BUILT UP AREA = 3627.00 SQ.FT.

PROPOSED SITE SHOWN IN RED

EXECUTANT **CLAIMANT**

27.07.2026 SK